Plattegrond appartement — fictief testvoorbeeld

Schaal 1:50 (A4) · maten in meters

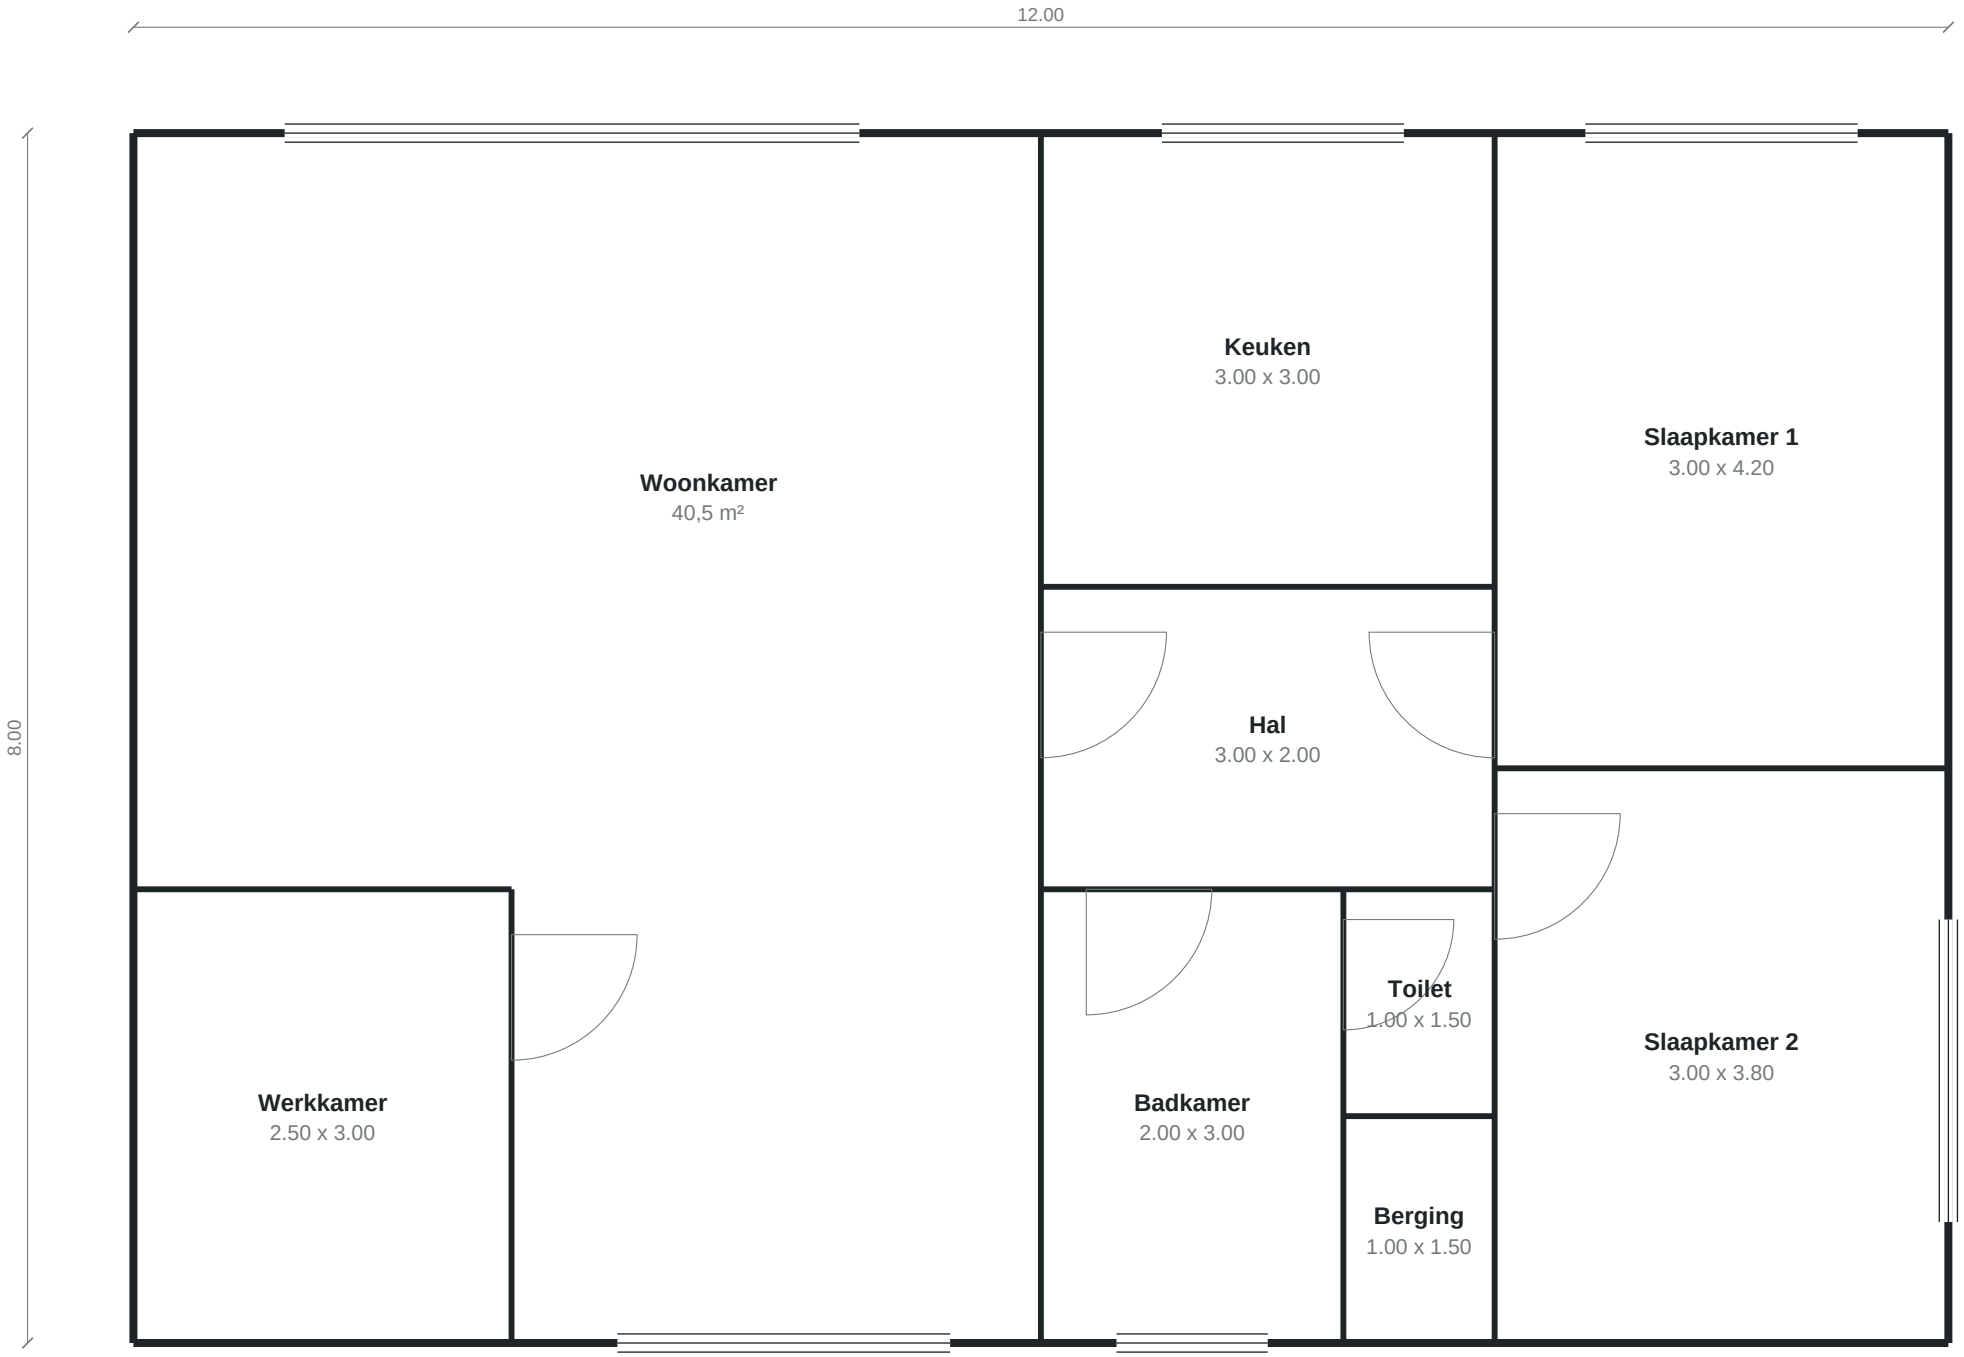

Zolder — fictief testvoorbeeld
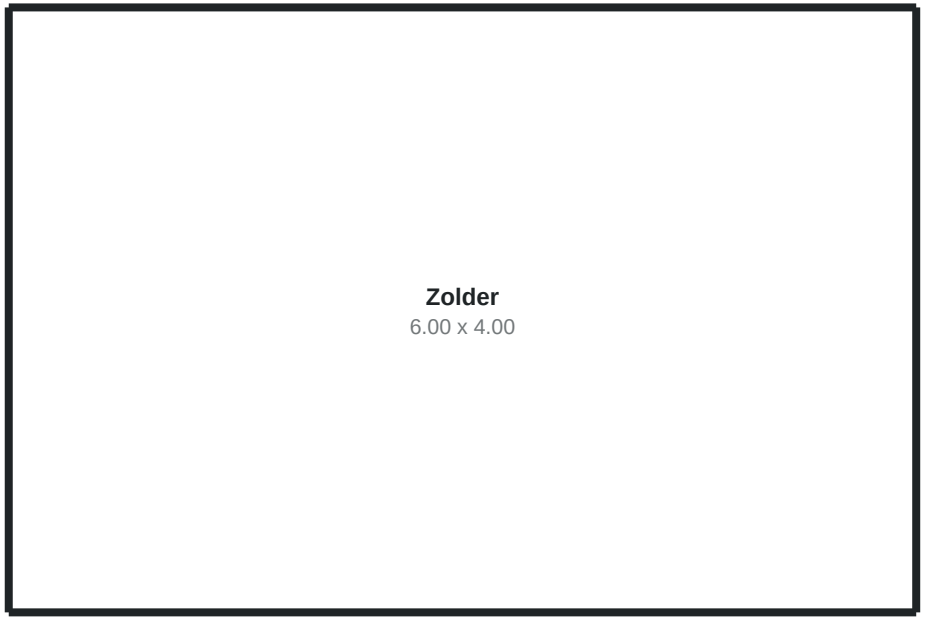
Schaal 1:50 (A4)